


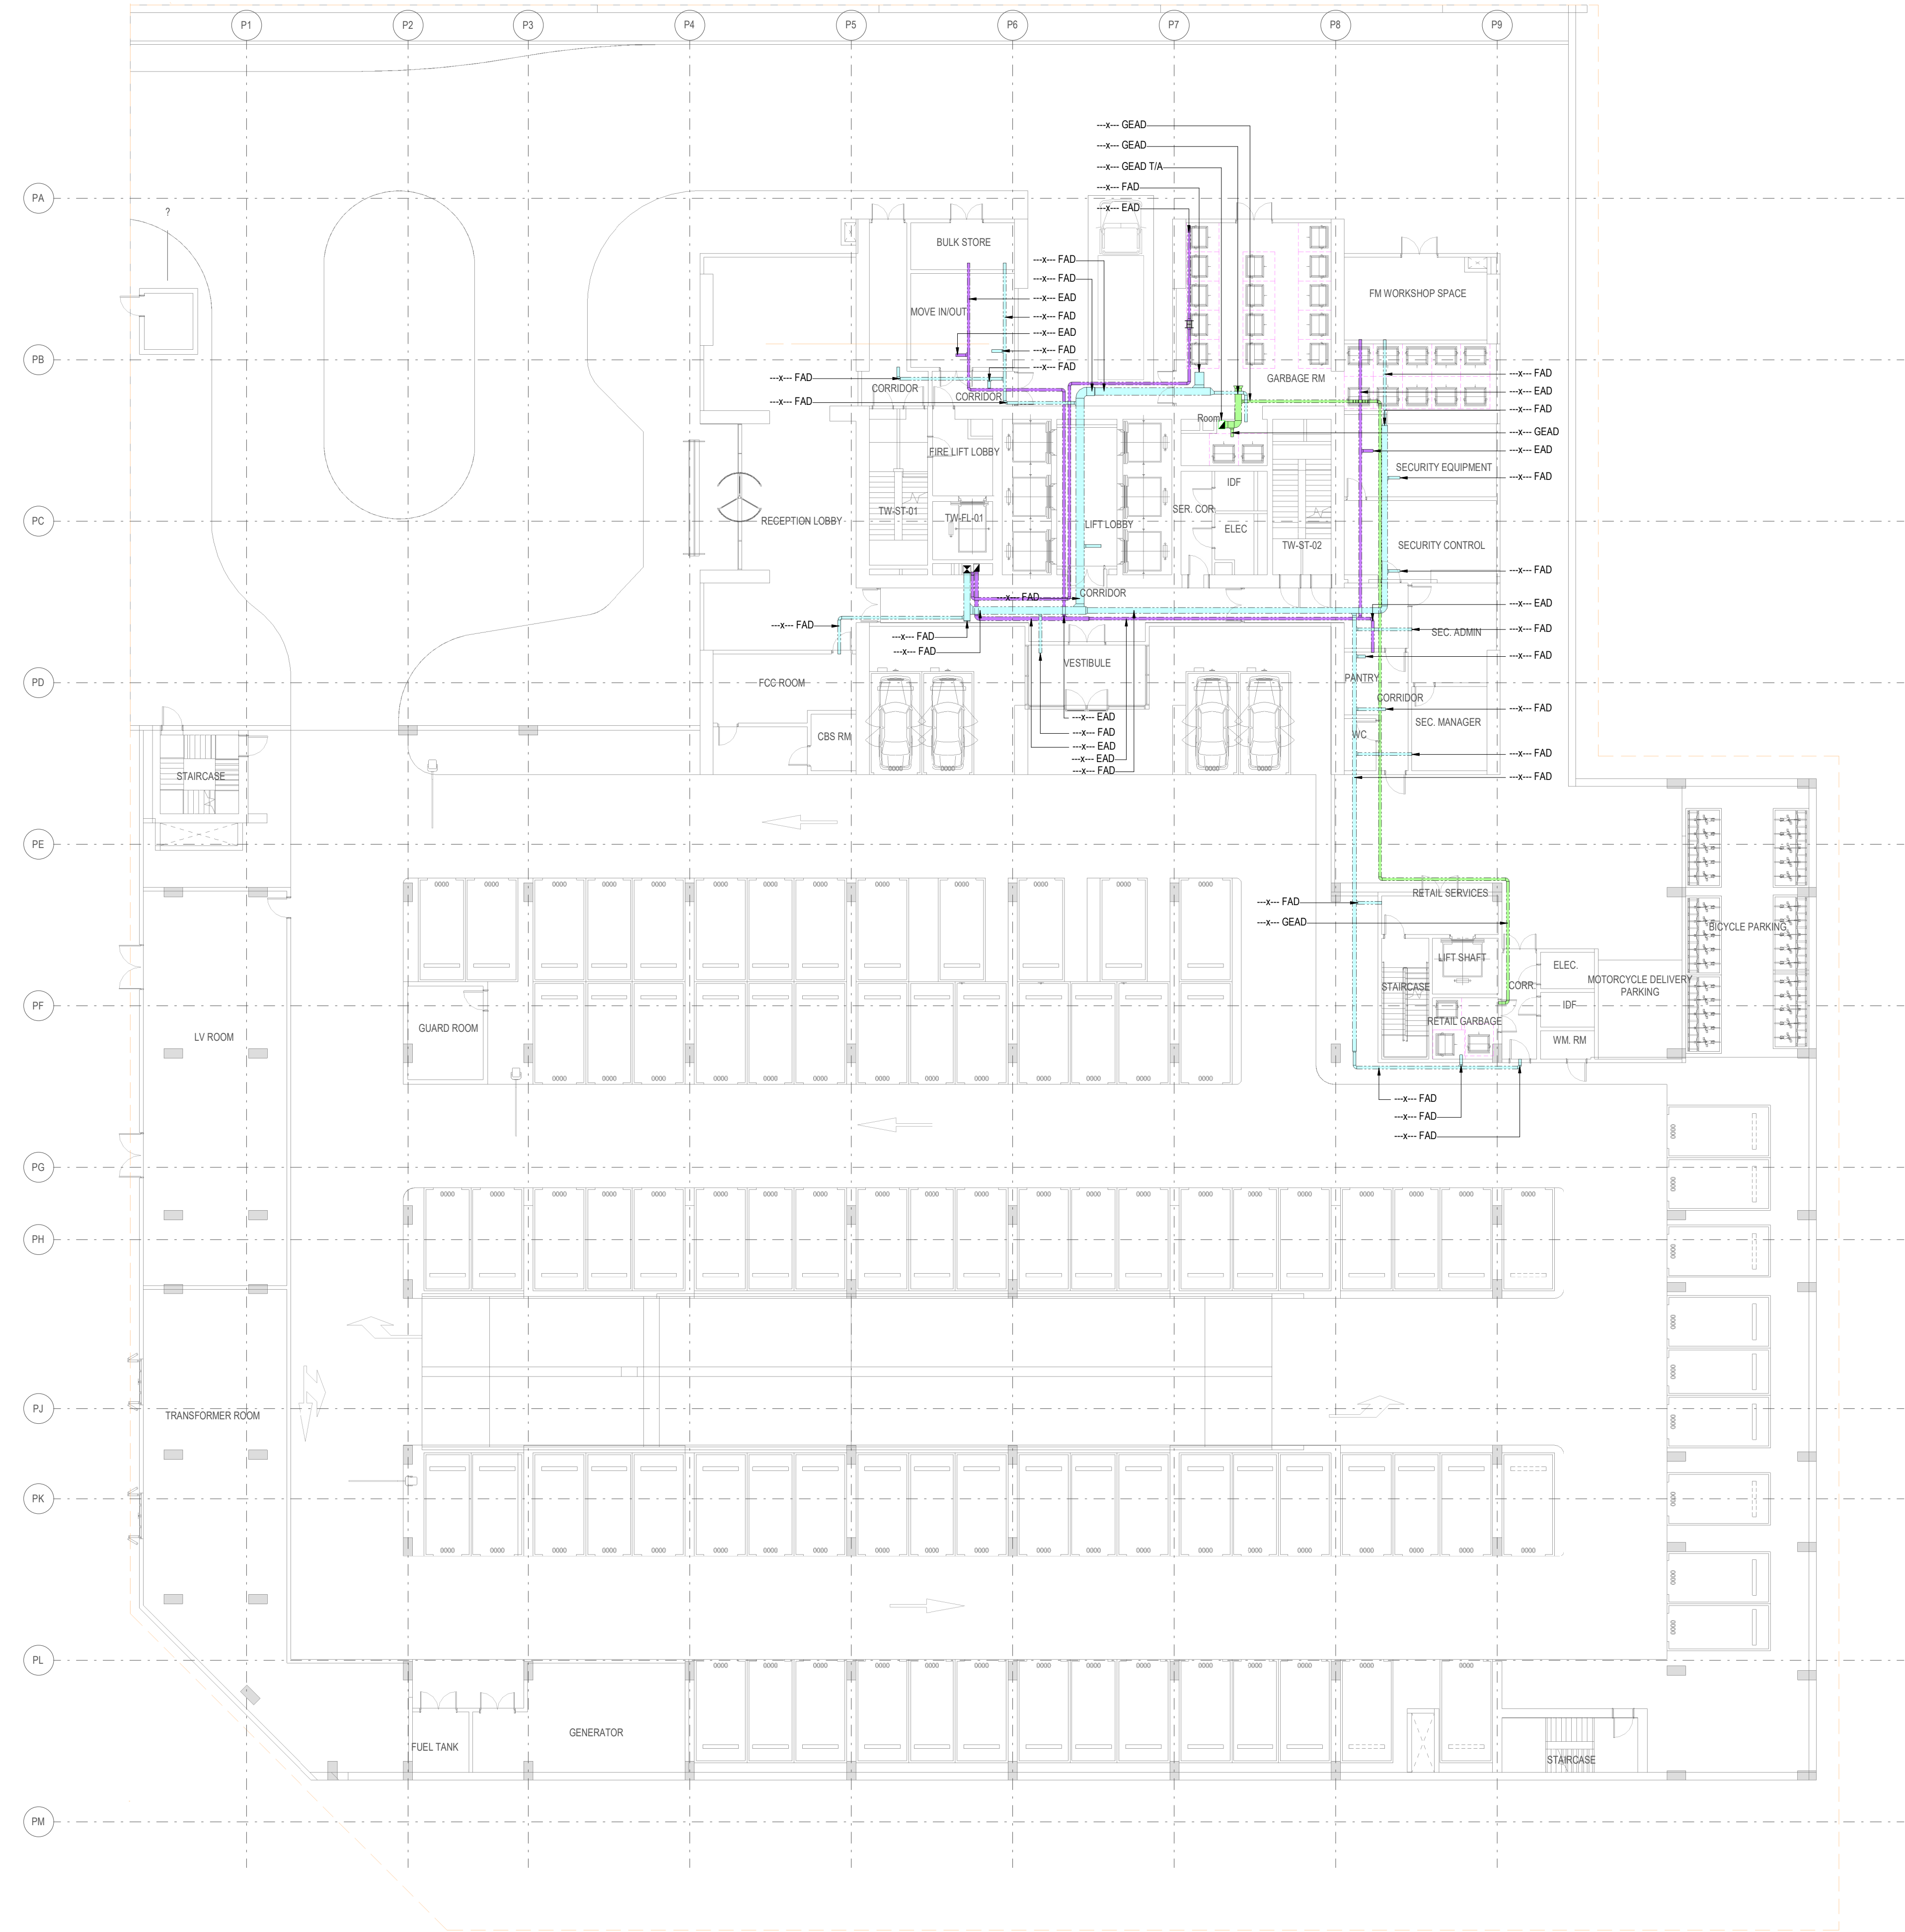

1 **GROUND FLOOR VENTILATION SYSTEM SERVICES SPACE PLANNING & LAYOUT**
2003 1 : 200

AUTHORITY STAMP

GENERAL NOTES:
1. THIS DRAWING IS THE COPYRIGHT OF MIRAGE LEISURE AND DEVELOPMENT AND MUST NOT BE RETAINED, COPIED, OR USED WITHOUT THE ABOVE CONSULTANT'S AUTHORITY.
2. DO NOT SCALE FROM THE DRAWINGS. CHECK ALL DIMENSIONS ON SITE AND NOTIFY THE ENGINEER OF ANY DISCREPANCIES BEFORE PROCEEDING WITH WORK.
3. ALL DIMENSIONS ARE IN MILLIMETERS AND LEVELS IN METERS, UNLESS NOTED OTHERWISE. ALL DIMENSIONS TO BE VERIFIED ON SITE AND APPROVED BY THE ENGINEER.
4. THIS DRAWING SHOULD BE READ IN CONJUNCTION WITH OTHER RELEVANT ARCHITECTURAL, STRUCTURAL, MECHANICAL, ELECTRICAL, CIVIL DRAWINGS, AND ALL RELEVANT SECTIONS OF THE SPECIFICATIONS.
ALL LEVELS SHOWN ARE CONSIDERING: +00.000 M DATUM LEVEL (WEST)

BUILDING PLOT NUMBER
4150465
KEY PLAN

TRUE NORTH
QIBLA

A	100% CONCEPT DESIGN SUBMISSION	14 AUG 2026	SK		
REV	DESCRIPTION	DATE	APPROVED BY		
PROJECT STAGE	CONCEPT DESIGN				
SHEET STATUS	FOR APPROVAL				
CLIENT	EMAAR				
LEAD DESIGN CONSULTANT AND ARCHITECT OF RECORD	mirage Mirage Inc Consultants, PO Box 54094, Emara Business Park, Office 302, Dubai, UAE T: +975 4 453 9535 W: www.mirageglobal.com				
SUBCONSULTANT					
DISCIPLINE	MECHANICAL				
PROJECT NAME	DCH-F14 DUBAI CREEK HARBOUR, DUBAI, UNITED ARAB EMIRATES				
SHEET NAME	PODIUM GROUND FLOOR VENTILATION SYSTEM SERVICES SPACE PLANNING & LAYOUT				
SCALE	ORIGINAL SHEET SIZE	MIRAGE PROJECT NUMBER			
1 : 200	ISO A1 (841x594mm)	DES00998			
AUTHORITY DRAWING NO.	MIRAGE DRAWING NO.	DRAWN BY	CHECKED BY	REVISION	
2003	2003	DG	JA	A	
SHEET NUMBER	DCH-F14-MRG-DRW-PDM-GFL-MHV-2003				