


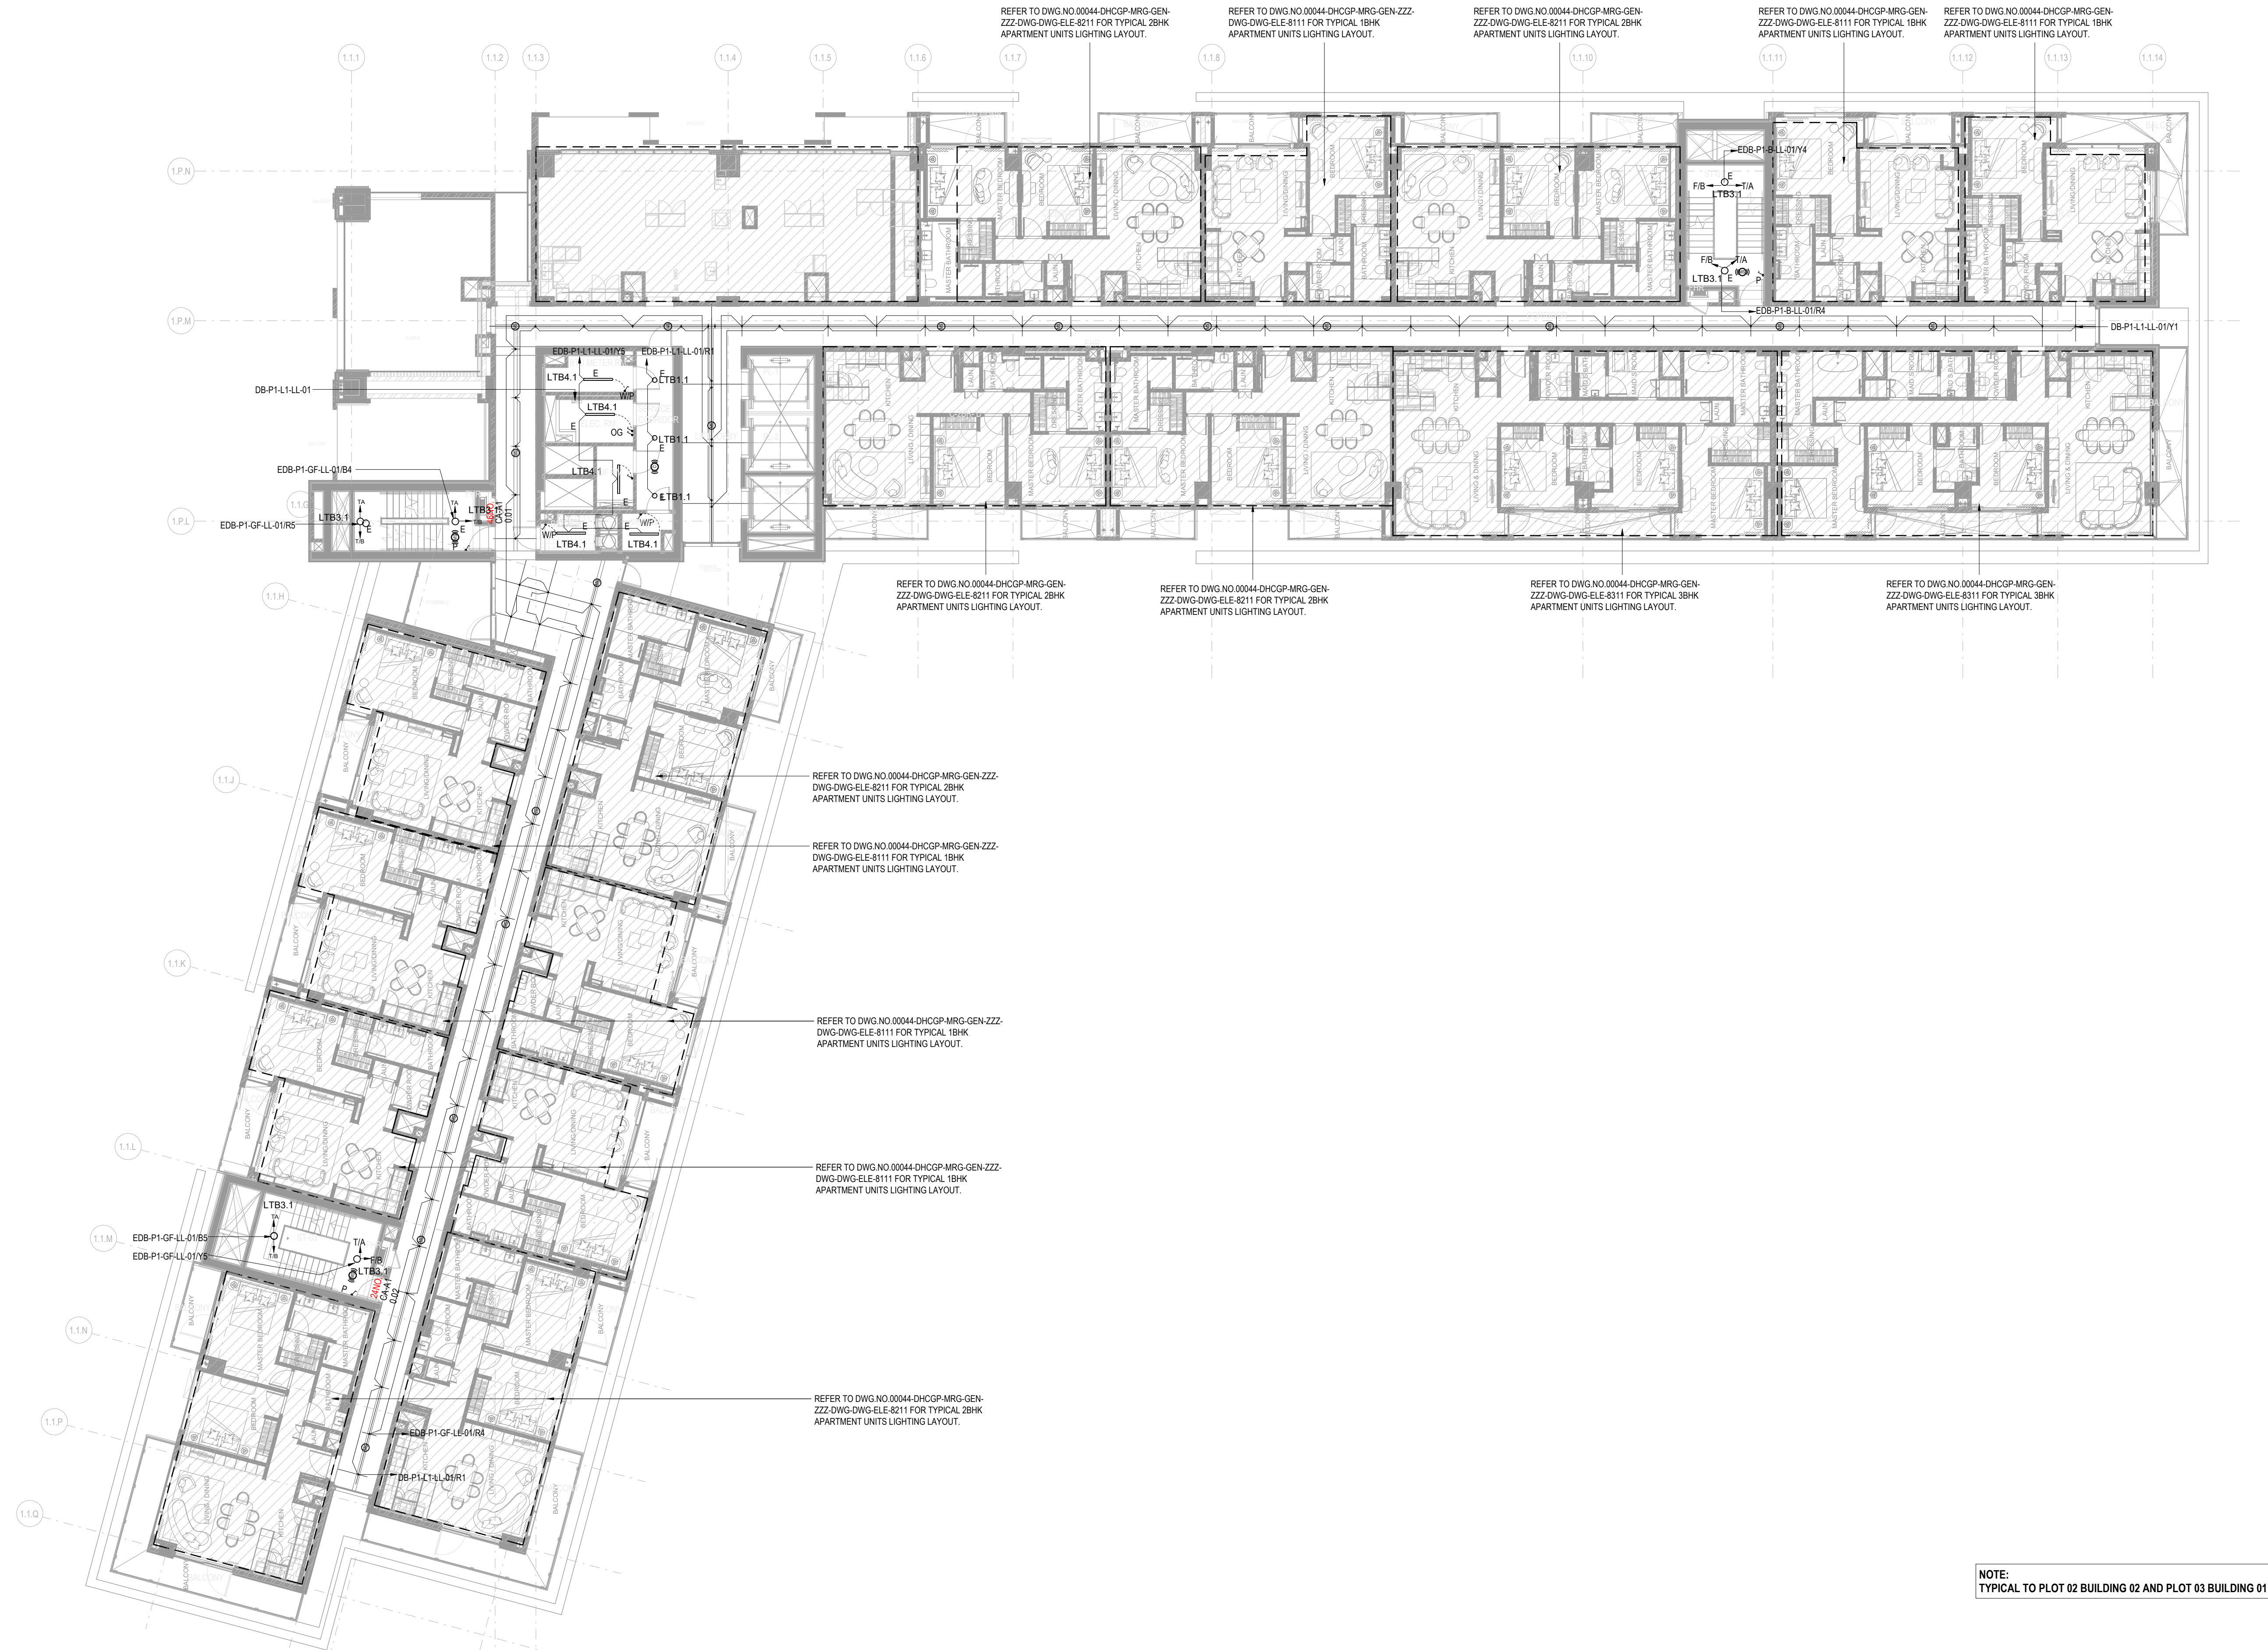


1 BD1 - 1ST FLOOR LIGHTING LAYOUT
1: 150

NOTE:
TYPICAL TO PLOT 02 BUILDING 02 AND PLOT 03 BUILDING 01

AUTHORITY STAMP

- GENERAL NOTES:**
1. THIS DRAWING IS THE COPYRIGHT OF MIRAGE AND MUST NOT BE RETAINED, COPIED, OR USED WITHOUT THE ABOVE CONSULTANTS' AUTHORITY.
 2. DO NOT SCALE FROM THE DRAWINGS. CHECK ALL DIMENSIONS ON SITE AND NOTIFY THE ENGINEER OF ANY DISCREPANCIES BEFORE PROCEEDING WITH WORK.
 3. ALL DIMENSIONS ARE IN MILLIMETERS AND LEVELS IN METERS, UNLESS NOTED OTHERWISE. ALL DIMENSIONS TO BE VERIFIED ON SITE AND APPROVED BY THE ENGINEER.
 4. THIS DRAWING SHOULD BE READ IN CONJUNCTION WITH OTHER RELEVANT ARCHITECTURAL, STRUCTURAL, MECHANICAL, ELECTRICAL, CIVIL DRAWINGS, AND ALL RELEVANT SECTIONS OF THE SPECIFICATIONS.
 5. THE FLOOR LEVEL 0.000 IS EQUAL TO +6.50 M RELATIVE TO THE DM DATUM LEVEL.


BUILDING PLOT NUMBER
3262969 - 01
KEY PLAN

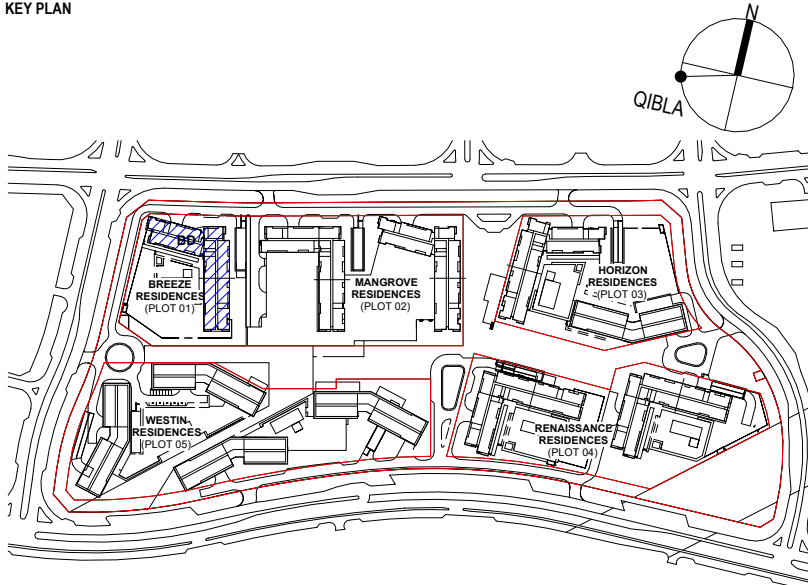

REV	DESCRIPTION	DATE	APPROVED BY
A	100% DETAIL DESIGN	11-SEP-2026	AV

PROJECT STAGE
DETAIL DESIGN

SHEET STATUS
FOR APPROVAL

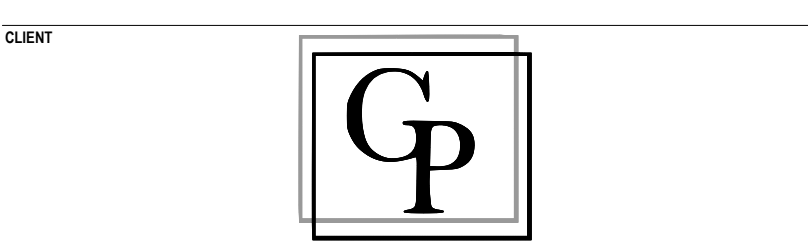

LEAD DESIGN CONSULTANT AND ARCHITECT OF RECORD
mirage
Mirage Inc Consultants, PO Box 54094, Emisar Business Park, Office 302, Dubai, UAE
T: +971 4 453 9835 W: www.mirageglobal.com

SUBCONSULTANT

DISCIPLINE
ELECTRICAL

PROJECT NAME
**DUBAI CREEK GARDENS
BREEZE RESIDENCES (PLOT 01)
AL JADDAF, DUBAI
UNITED ARAB EMIRATES**

SHEET NAME
**BD1
1ST FLOOR
LIGHTING LAYOUT**

SCALE	ORIGINAL SHEET SIZE	MIRAGE PROJECT NUMBER	REVISION
1: 150	ISO A1 (841x594mm)	DES00944	
AUTHORITY DRAWING NO. E-00-1101	MIRAGE DRAWING NO. E-1101	DRAWN BY MM	CHECKED BY MC
SHEET NUMBER 00044-DHCGP-MRGP-PL1-BD1-DWG-ELE-1101		REVISION A	