

2. DO NOT SCALE FROM THE DRAWINGS. CHECK ALL DIMENSIONS ON SITE AND NOTIFY THE ENGINEER OF ANY DISCREPANCIES BEFORE PROCEEDING WITH WORK.

3. ALL DIMENSIONS ARE IN MILLIMETERS AND LEVELS IN METERS, UNLESS NOTED OTHERWISE. ALL DIMENSIONS TO BE VERIFIED ON SITE AND APPROVED BY THE ENGINEER.


4. THIS DRAWING SHOULD BE READ IN CONJUNCTION WITH OTHER RELEVANT ARCHITECTURAL, STRUCTURAL, MECHANICAL, ELECTRICAL, CIVIL DRAWINGS, AND ALL RELEVANT SECTIONS OF THE SPECIFICATIONS.

5. THE FLOOR LEVEL 0.000 IS EQUAL TO +6.50 M RELATIVE TO THE DM DATUM LEVEL

BUILDING PLOT NUMBER

3262969 - 0

KEY PLAN

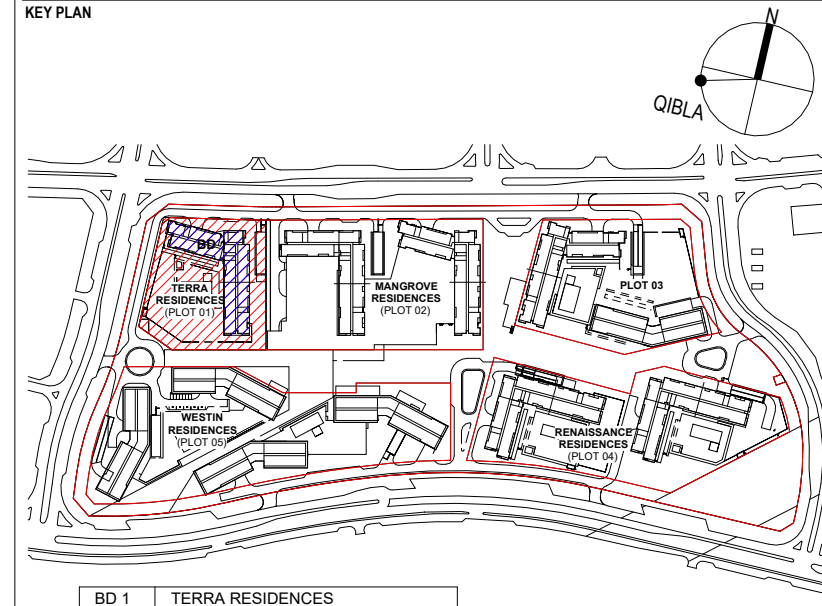


A	100% DETAIL DESIGN	11-SEP-2026	AV
REV	DESCRIPTION	DATE	APPROVED

PROJECT STAGE	DETAIL DESIGN
---------------	---------------

FOR APPROVAL

CLIN

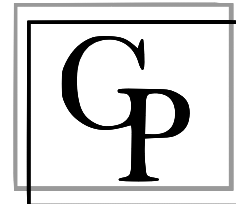

LEAD DESIGN CONSULTANT AND ARCHITECT OF RECORD

mirage

Mirage Inc Consultants, PO Box 54094, Emaar Business Park, Office 302, Dubai, U
T: +971 4 453 8835 W: www.mirageglobal.com

SUBCONSULTANT

DISCIPLIN

ELECTRICAL


PROJECT NAME

**DUBAI CREEK GARDENS
TERRA RESIDENCES (PLOT 01)
AL JADDAF, DUBAI
UNITED ARAB EMIRATES**

SHEET NAME

BD1
7TH FLOOR
(TYP. 8TH TO 9TH FLR.) LIGHTING LAYOUT

SCALE	ORIGINAL SHEET SIZE	MIRAGE PROJECT NUMBER		
1 : 150	ISO A1 (841x594mm)	DES00044		
AUTHORITY DRAWING NO.	MIRAGE DRAWING NO.	DRAWN BY	CHECKED BY	REVISION
E-00-1107	E-1107	MM	MC	A
SHEET NUMBER				
00044-DHCGP-MRG-PL1-BD1-DWG-FILE-1107				

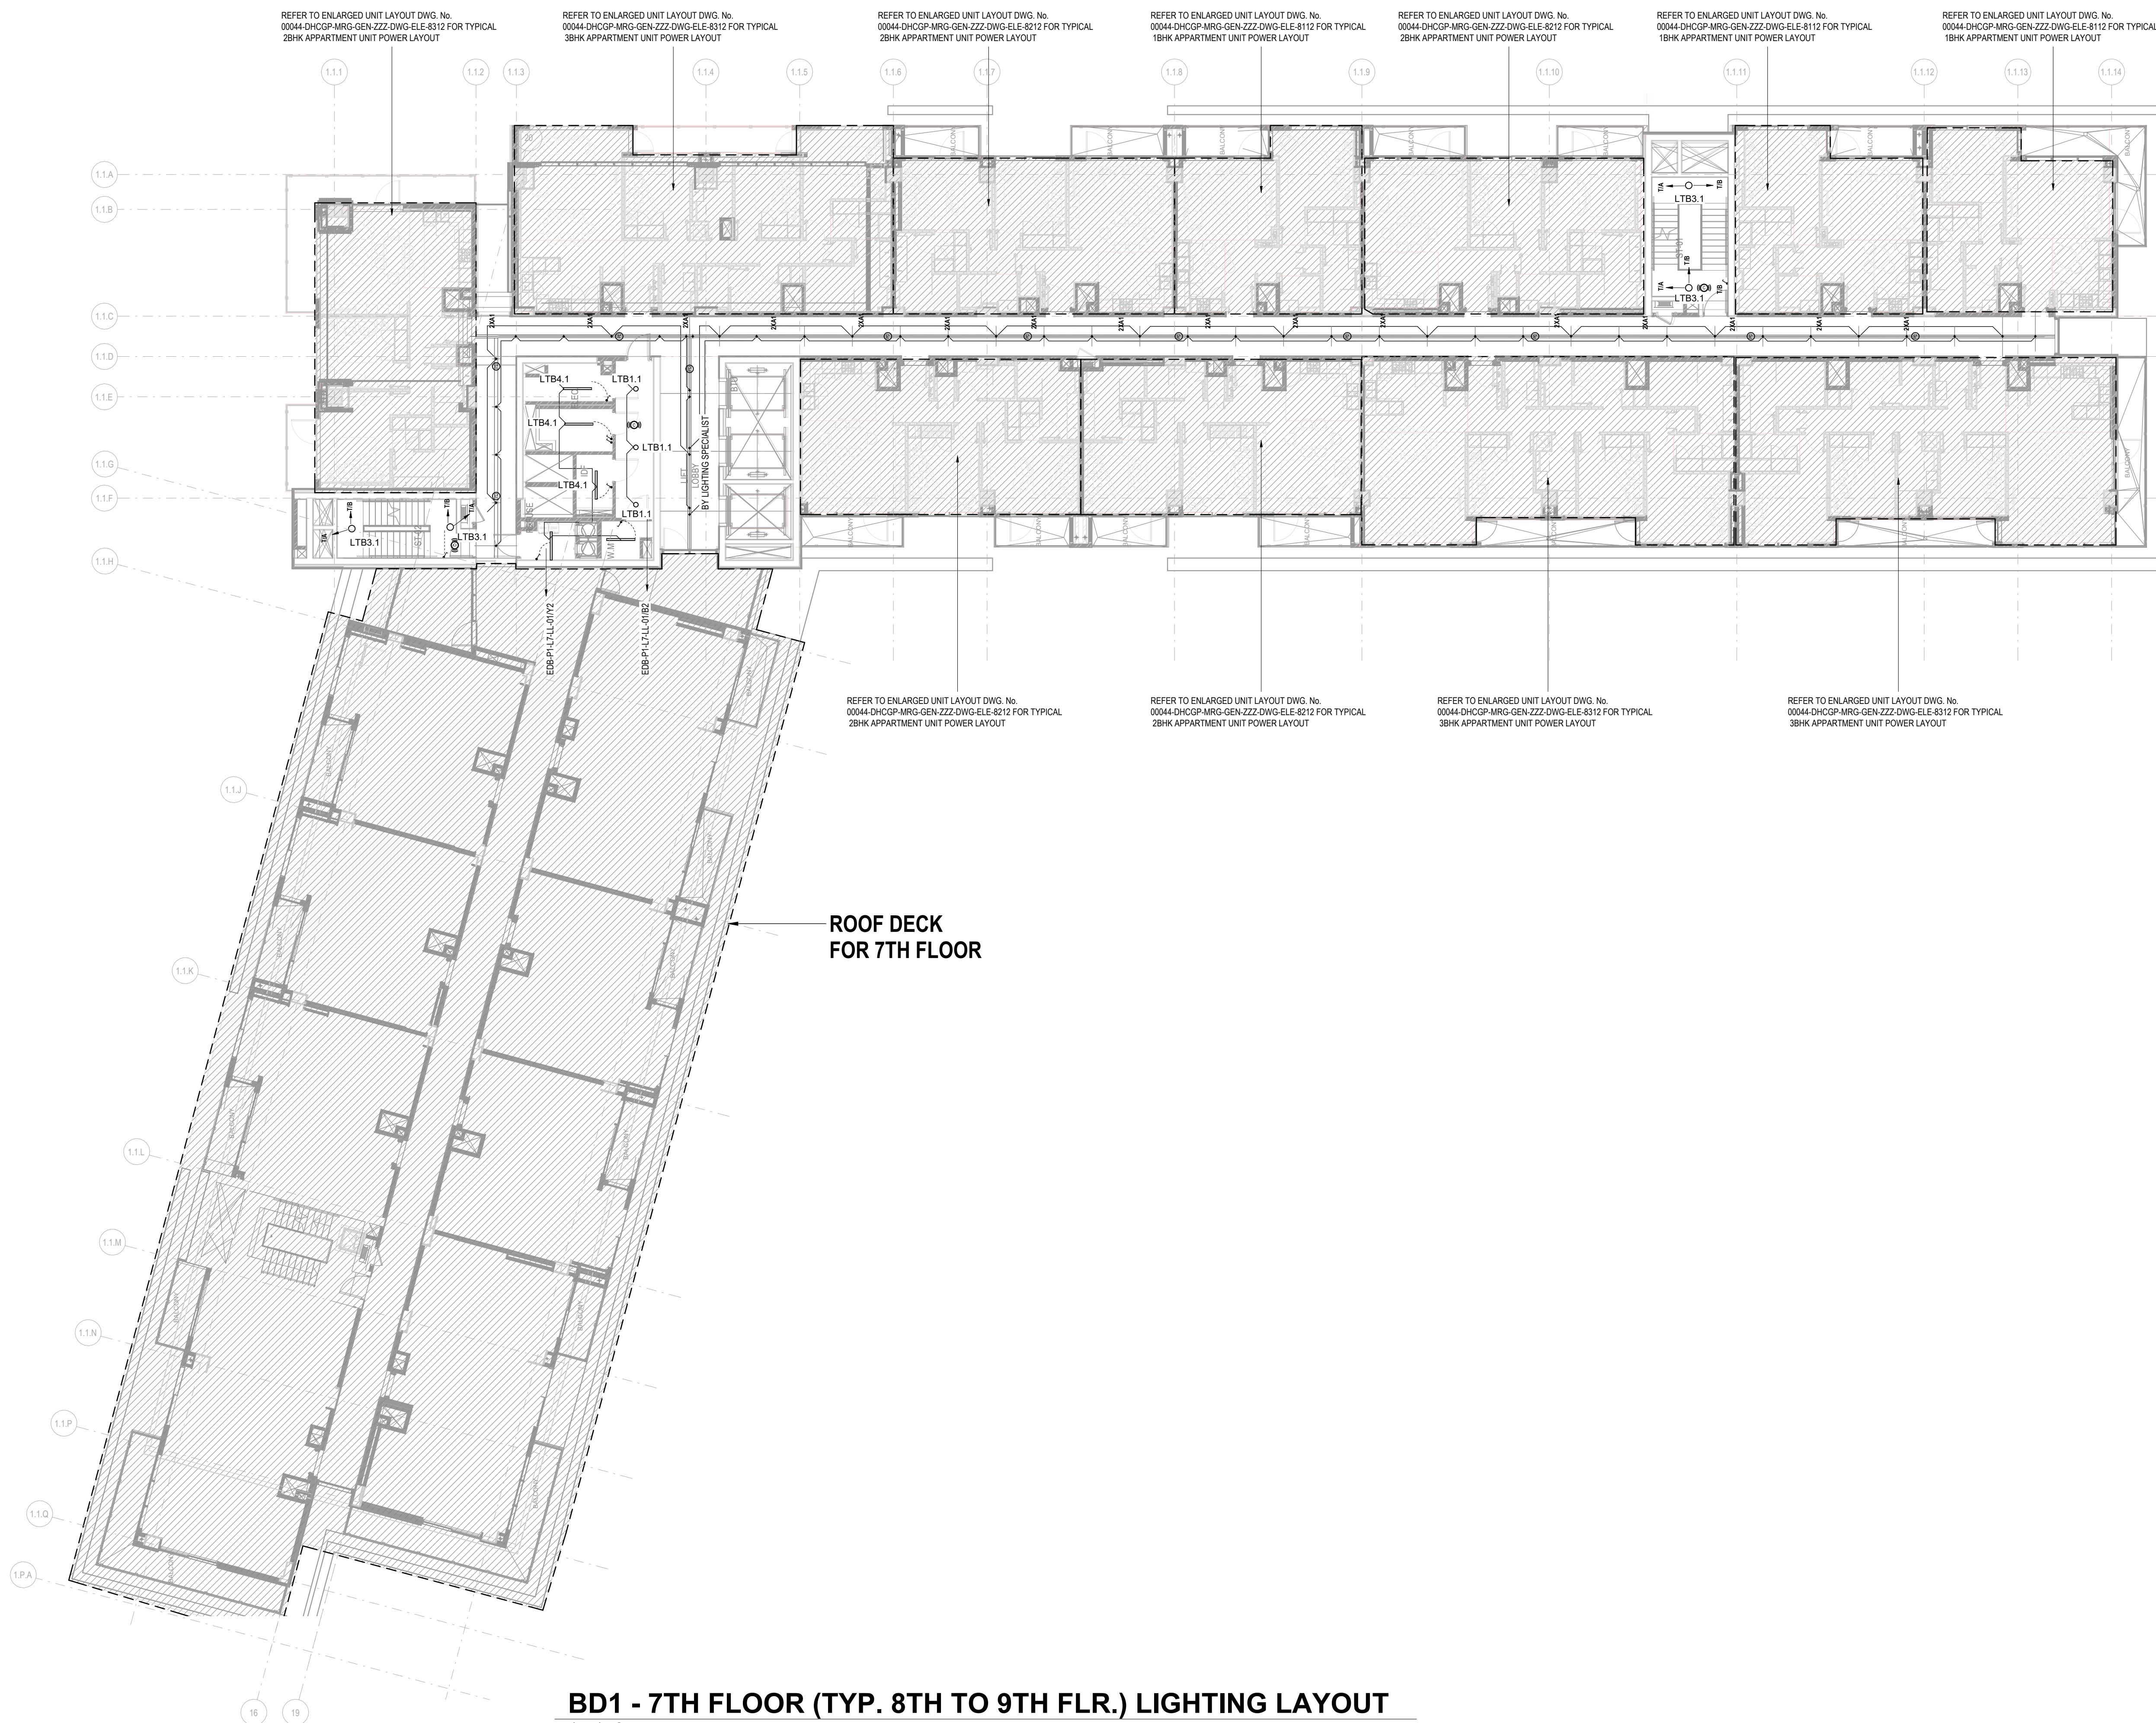

BD1 - 7TH FLOOR (TYP. 8TH TO 9TH FLR.) LIGHTING LAYOUT

1 : 150