



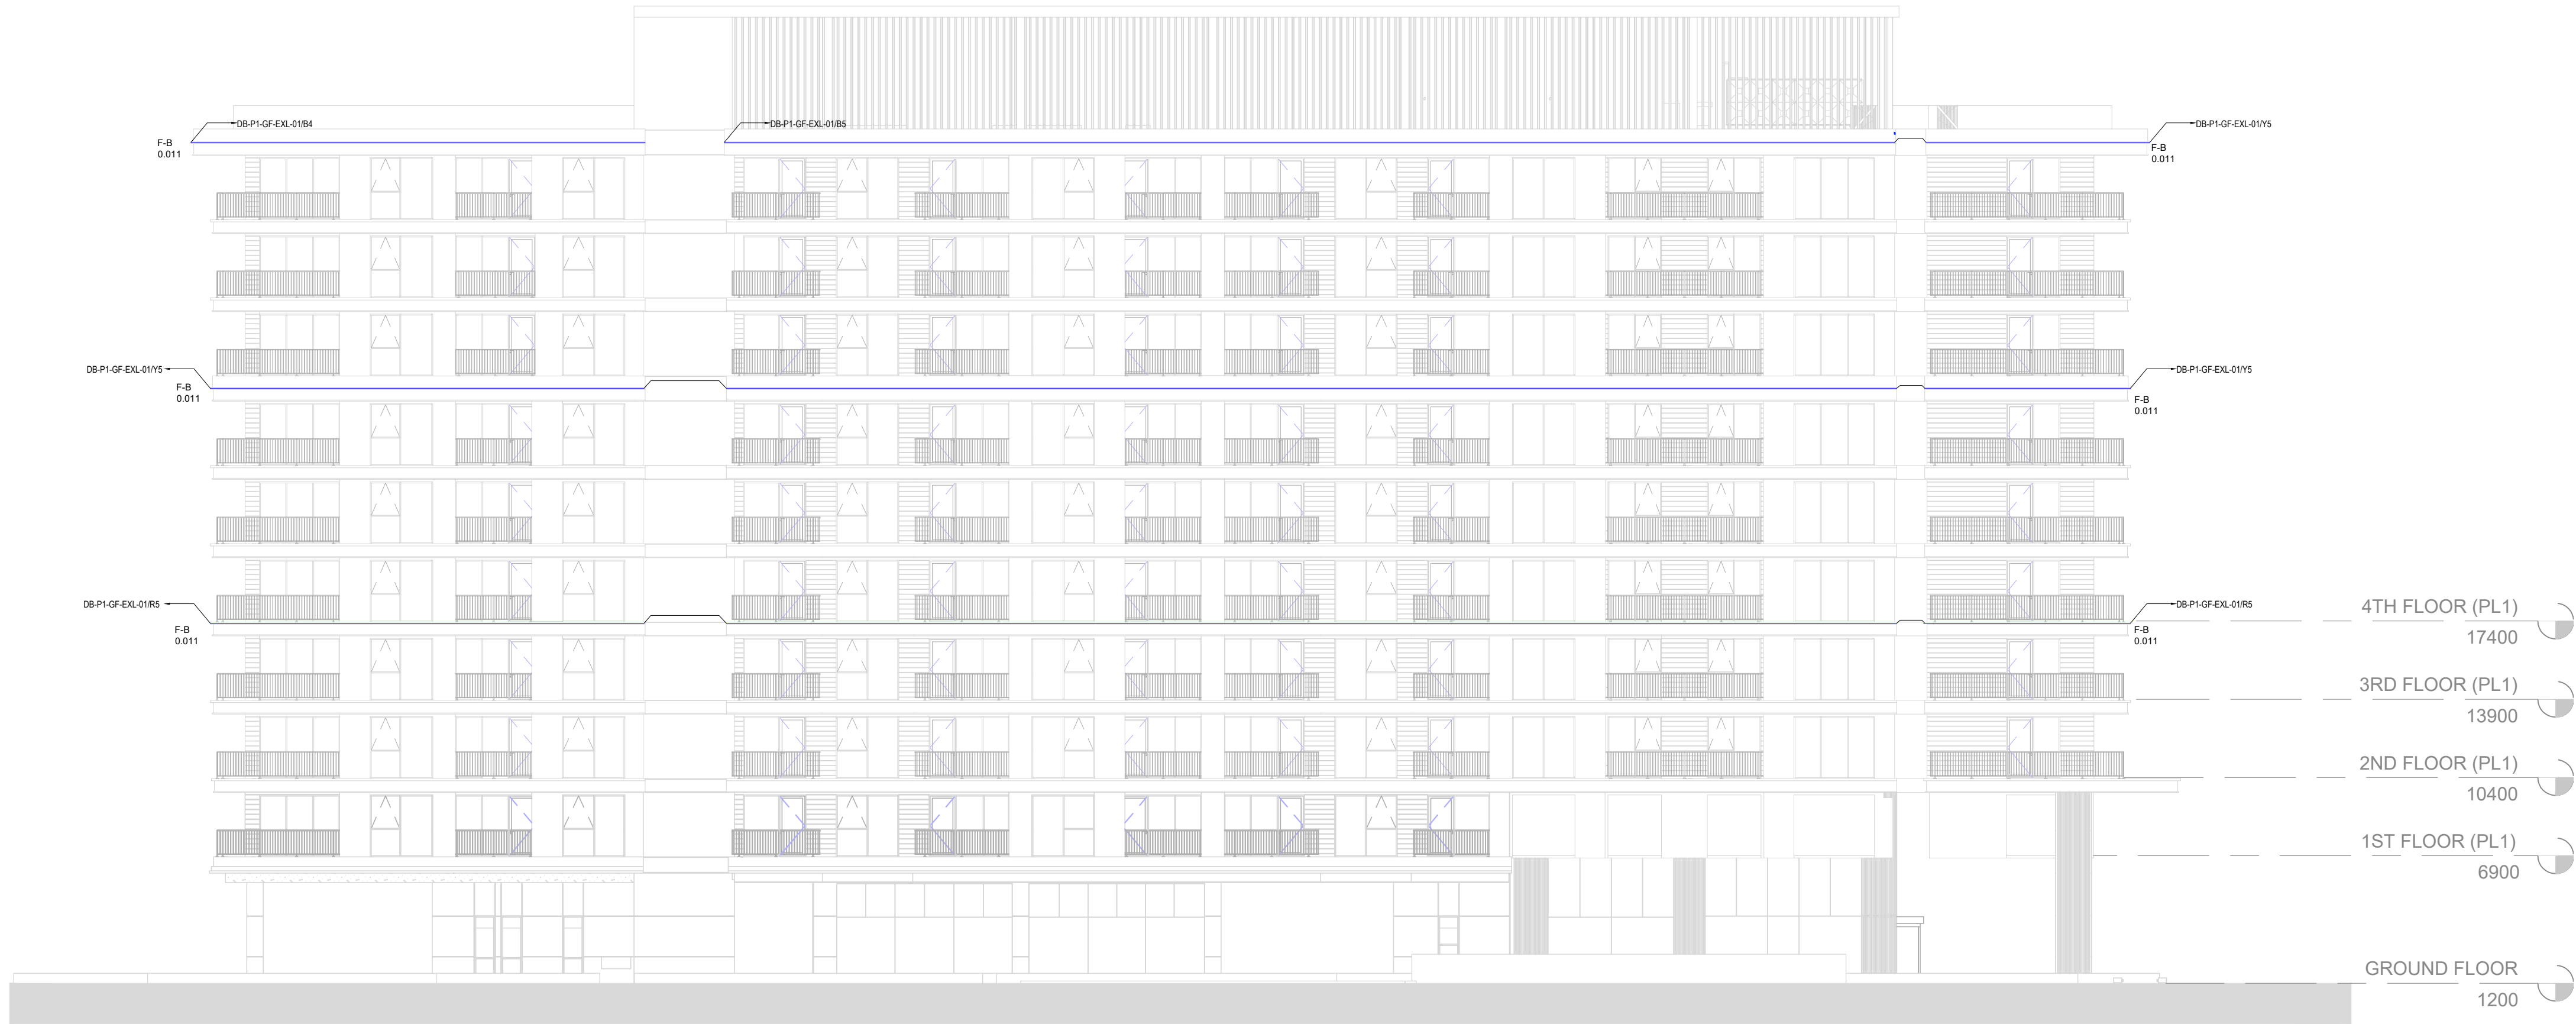


1 EAST FACADE
1 : 200

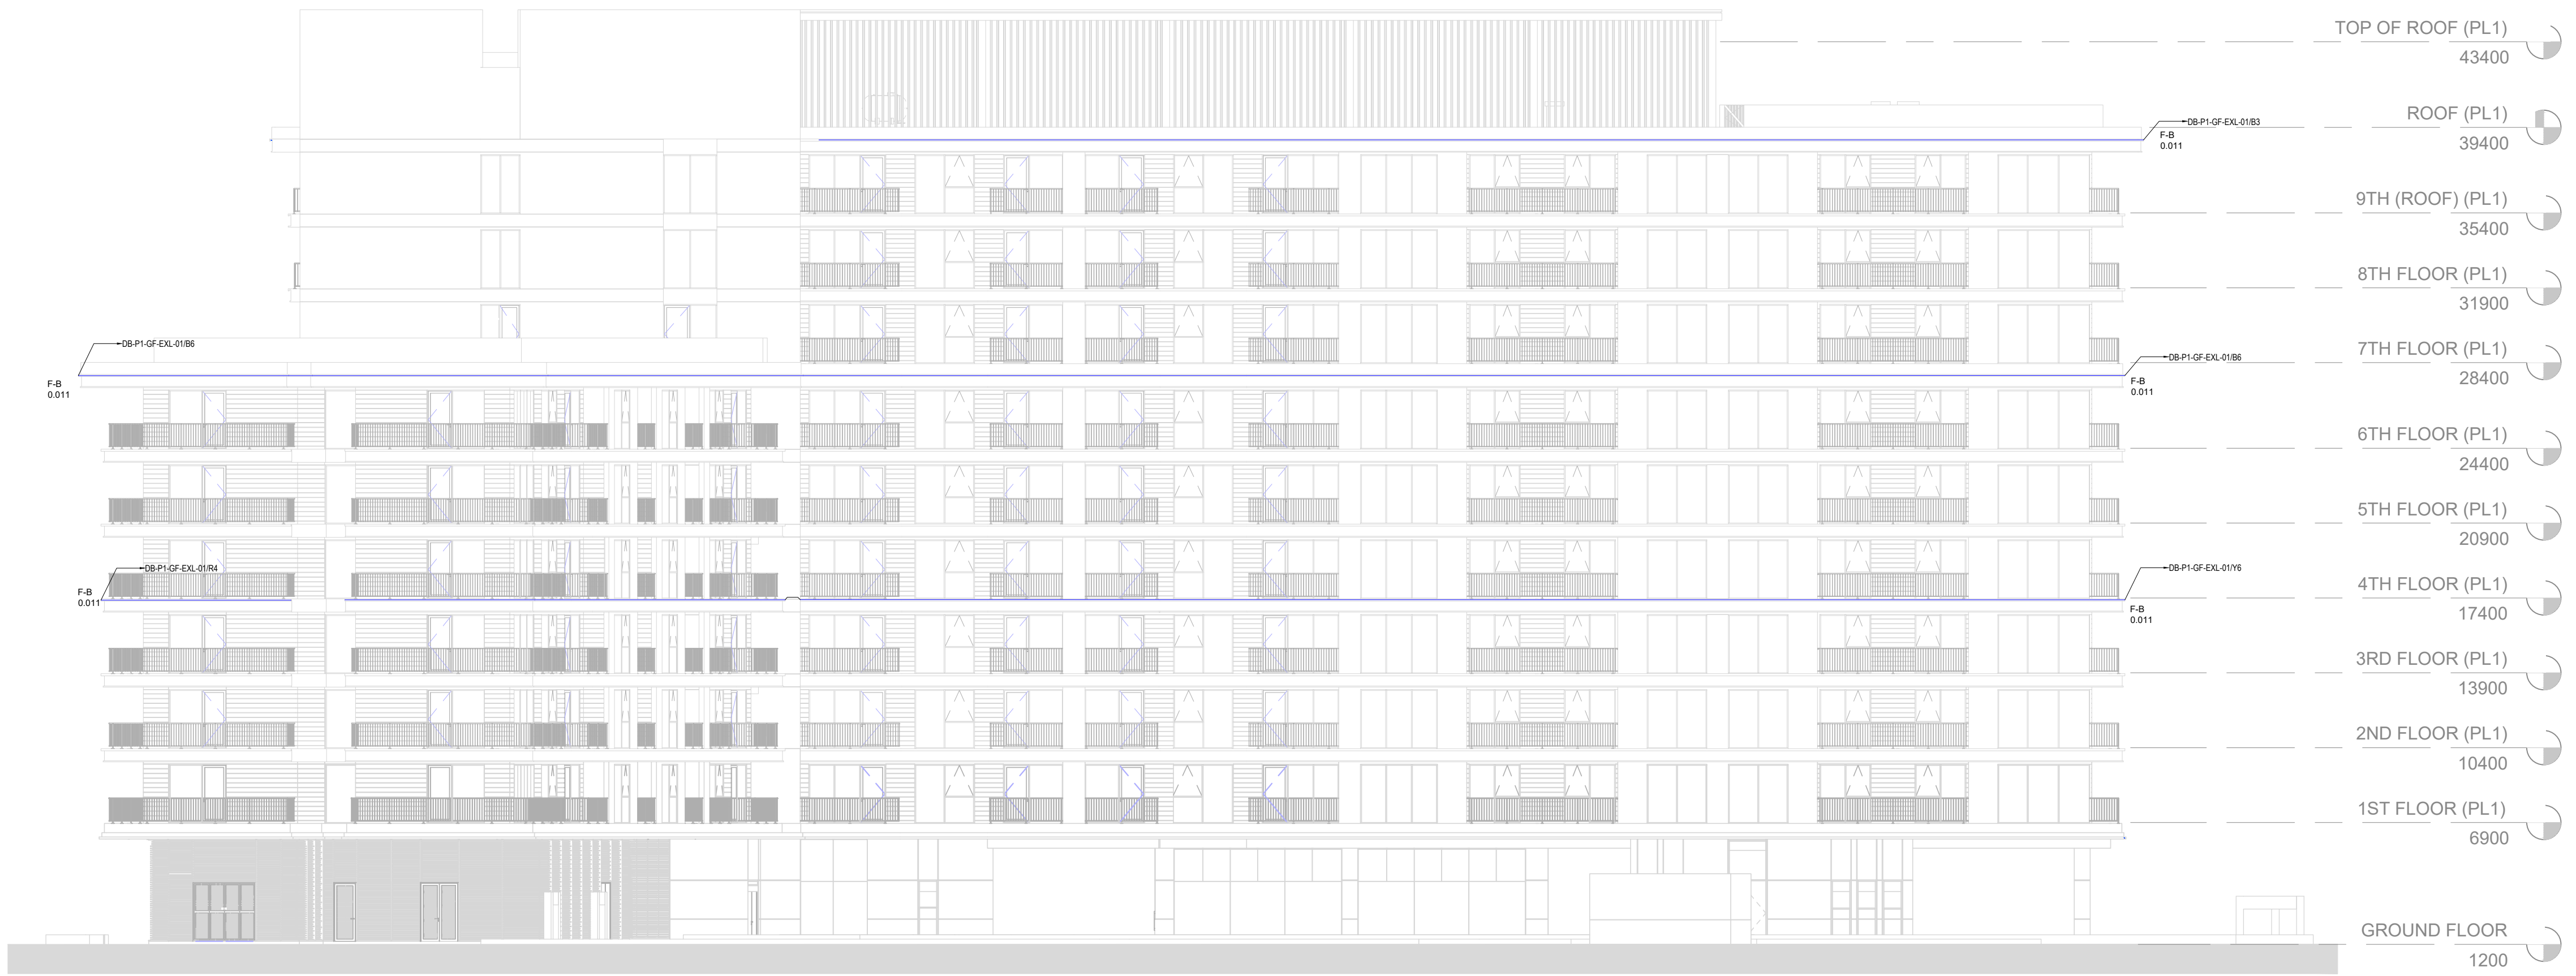

2 WEST FACADE
1 : 200

- AUTHORITY STAMP
- GENERAL NOTES:**
1. THIS DRAWING IS THE COPYRIGHT OF MIRAGE AND MUST NOT BE RETAINED, COPIED, OR USED WITHOUT THE ABOVE CONSULTANTS' AUTHORITY.
 2. DO NOT SCALE FROM THE DRAWINGS. CHECK ALL DIMENSIONS ON SITE AND NOTIFY THE ENGINEER OF ANY DISCREPANCIES BEFORE PROCEEDING WITH WORK.
 3. ALL DIMENSIONS ARE IN MILLIMETERS AND LEVELS IN METERS, UNLESS NOTED OTHERWISE. ALL DIMENSIONS TO BE VERIFIED ON SITE AND APPROVED BY THE ENGINEER.
 4. THIS DRAWING SHOULD BE READ IN CONJUNCTION WITH OTHER RELEVANT ARCHITECTURAL, STRUCTURAL, MECHANICAL, ELECTRICAL, CIVIL DRAWINGS, AND ALL RELEVANT SECTIONS OF THE SPECIFICATIONS.
 5. THE FLOOR LEVEL 0.000 IS EQUAL TO +6.25 M RELATIVE TO THE DM DATUM LEVEL.

BUILDING PLOT NUMBER
3262969 - 01
KEY PLAN

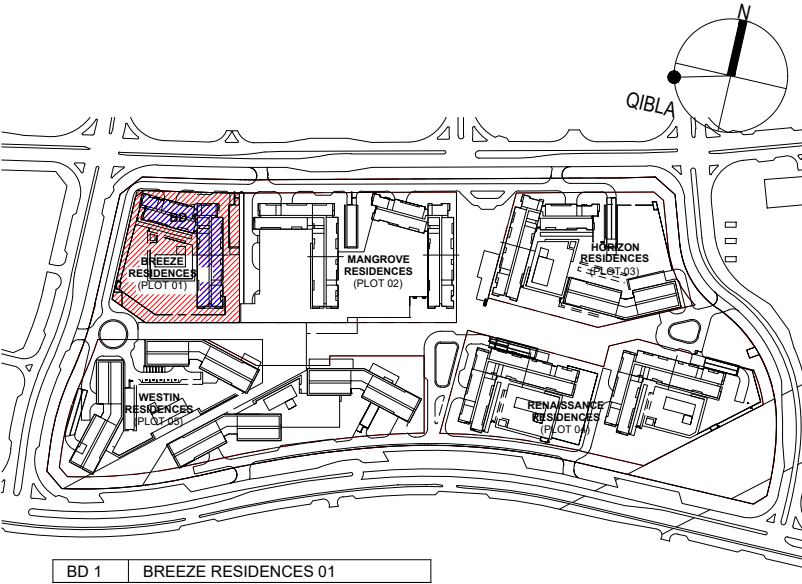

REV	DESCRIPTION	DATE	APPROVED BY
A	100% DETAIL DESIGN	11-SEP-2026	AV

PROJECT STAGE
DETAIL DESIGN

SHEET STATUS
FOR APPROVAL

CLIENT

LEAD DESIGN CONSULTANT AND ARCHITECT OF RECORD

Mirage Inc. Consultants, PO Box 54094, Emara Business Park, Office 302, Dubai, UAE
T: +971 4 453 9835 W: www.mirageglobal.com

SUBCONSULTANT

DISCIPLINE
ELECTRICAL

PROJECT NAME
**DUBAI CREEK GARDENS
BREEZE RESIDENCES (PLOT 01)
AL JADDAF, DUBAI
UNITED ARAB EMIRATES**

SHEET NAME
**FACADE LIGHTING LAYOUT
BREEZE RESIDENCES (PLOT 01)
BUILDING 1
ELEVATION 01 & 02**

SCALE	ORIGINAL SHEET SIZE	MIRAGE PROJECT NUMBER	DESIGN NUMBER	DRAWN BY	CHECKED BY	REVISION
1 : 200	ISO A1 (841x594mm)	DES00044	DES00044	MM	MC	A
AUTHORITY DRAWING NO.	MIRAGE DRAWING NO.					
X-XX-1112	X-1112					
SHEET NUMBER						
00044-DHCGP-MRG-PL1-BD1-DWG-ELE-1112						