


PART-1

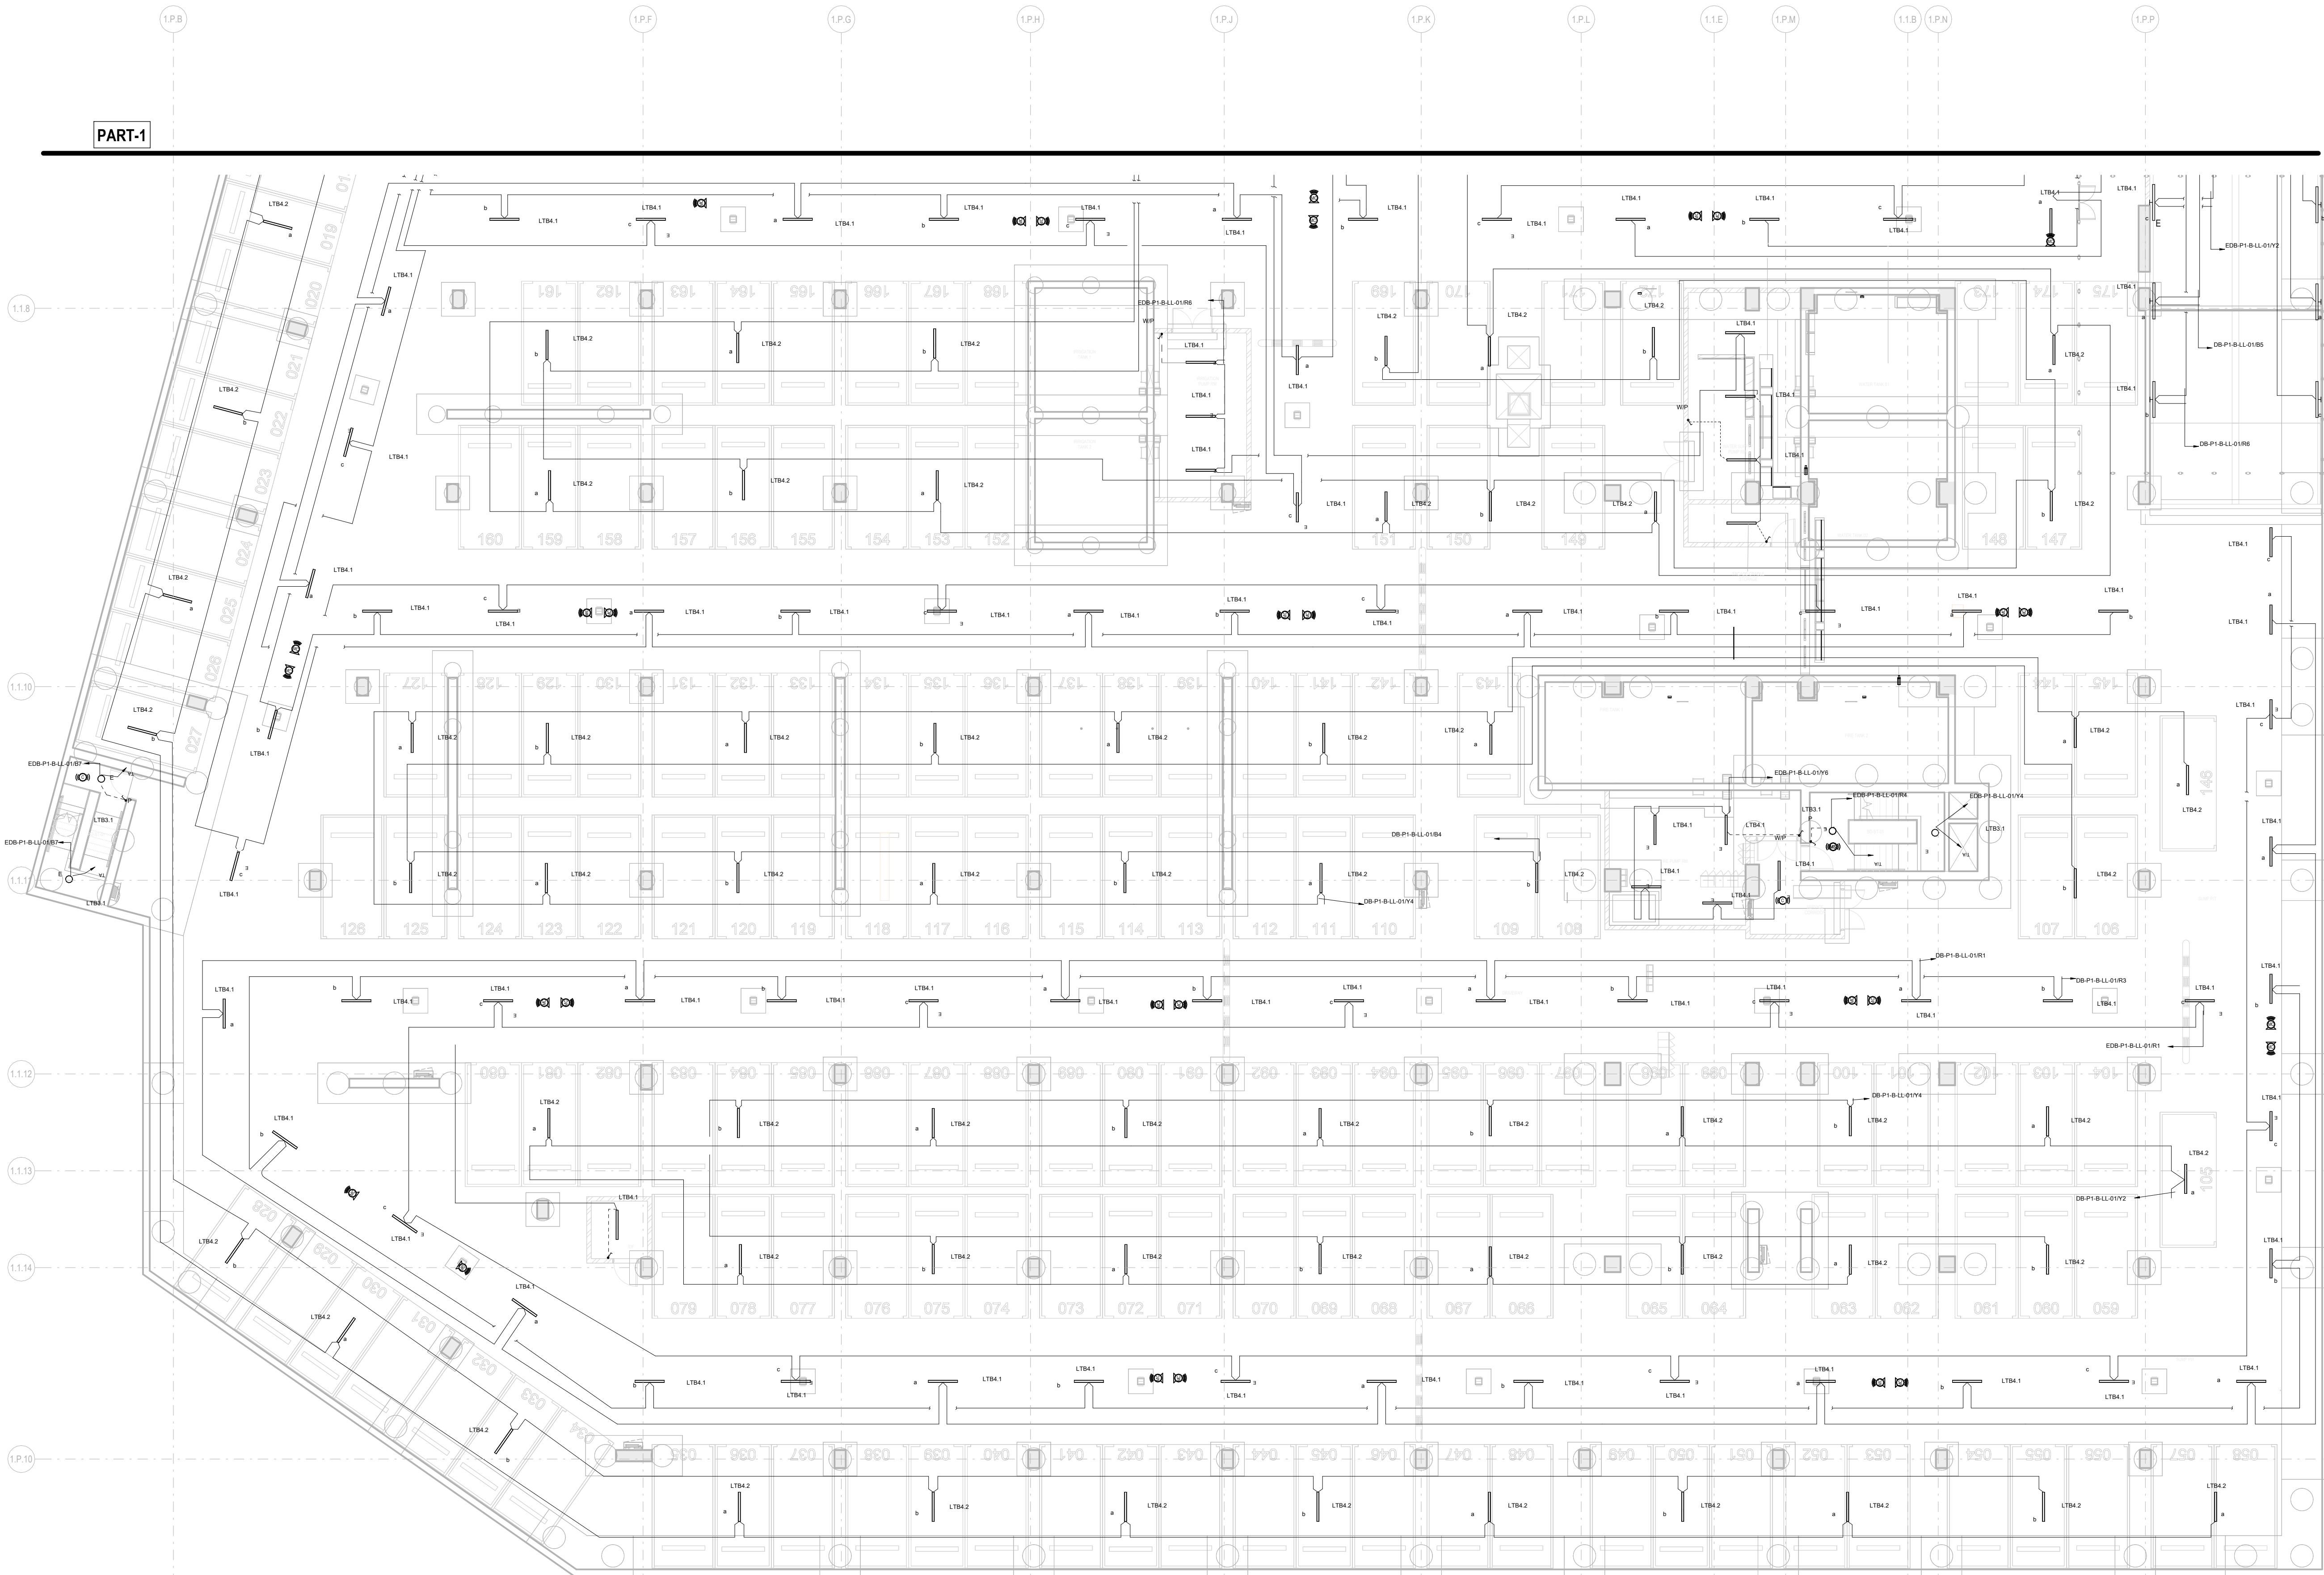


GENERAL NOTES:

1. THIS DRAWING IS THE COPYRIGHT OF MIRAGE AND MUST NOT BE RETAINED, COPIED, OR USED WITHOUT THE ABOVE CONSULTANTS' AUTHORITY.
2. DO NOT SCALE FROM THE DRAWINGS. CHECK ALL DIMENSIONS ON SITE AND NOTIFY THE ENGINEER OF ANY DISCREPANCIES BEFORE PROCEEDING WITH WORK.
3. ALL DIMENSIONS ARE IN MILLIMETERS AND LEVELS IN METERS, UNLESS NOTED OTHERWISE. ALL DIMENSIONS TO BE VERIFIED ON SITE AND APPROVED BY THE ENGINEER.
4. THIS DRAWING SHOULD BE READ IN CONJUNCTION WITH OTHER RELEVANT ARCHITECTURAL, STRUCTURAL, MECHANICAL, ELECTRICAL, CIVIL DRAWINGS, AND ALL RELEVANT SECTIONS OF THE SPECIFICATIONS.
5. THE FLOOR LEVEL 0.000 IS EQUAL TO +6.50 M RELATIVE TO THE DM DATUM LEVEL.

BUILDING PLOT NUMBER

3262969 - 01

KEY PLAN

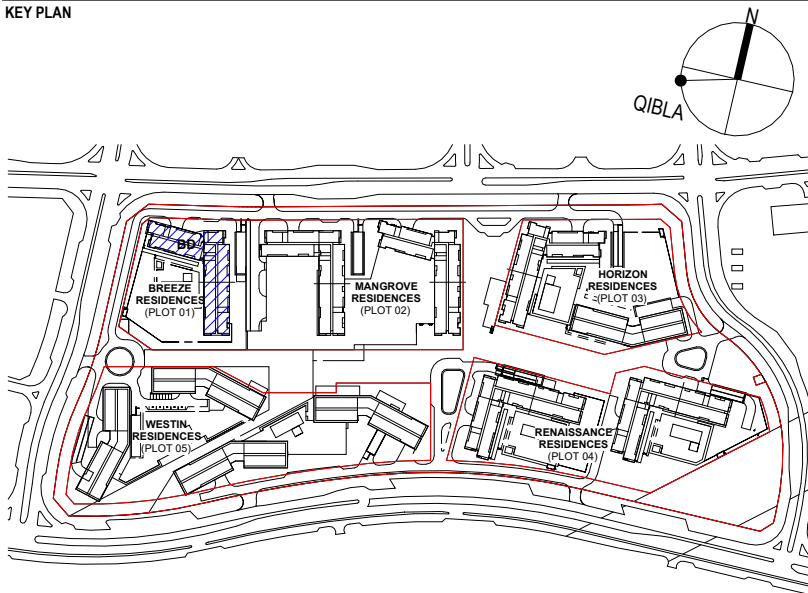

REV	DESCRIPTION	DATE	APPROVED BY
A	100% DETAIL DESIGN	11-SEP-2026	AV

PROJECT STAGE

DETAIL DESIGN

SHEET STATUS

FOR APPROVAL

CLIENT



LEAD DESIGN CONSULTANT AND ARCHITECT OF RECORD



SUBCONSULTANT

DISCIPLINE

ELECTRICAL

PROJECT NAME

DUBAI CREEK GARDENS
BREEZE RESIDENCES (PLOT 01)
AL JADDAF, DUBAI
UNITED ARAB EMIRATES

SHEET NAME

PODIUM
BASEMENT
LIGHTING LAYOUT SHEET 02

SCALE	ORIGINAL SHEET SIZE	MIRAGE PROJECT NUMBER	REVISION
1 : 150	ISO A1 (841x594mm)	DES00944	
AUTHORITY DRAWING NO.	MIRAGE DRAWING NO.	DRAWN BY	CHECKED BY
E-00-1002	E-1002	MM	MC
SHEET NUMBER	00044-DHCGP-MRG-PL-1-BSM-DWG-ELE-1002		