



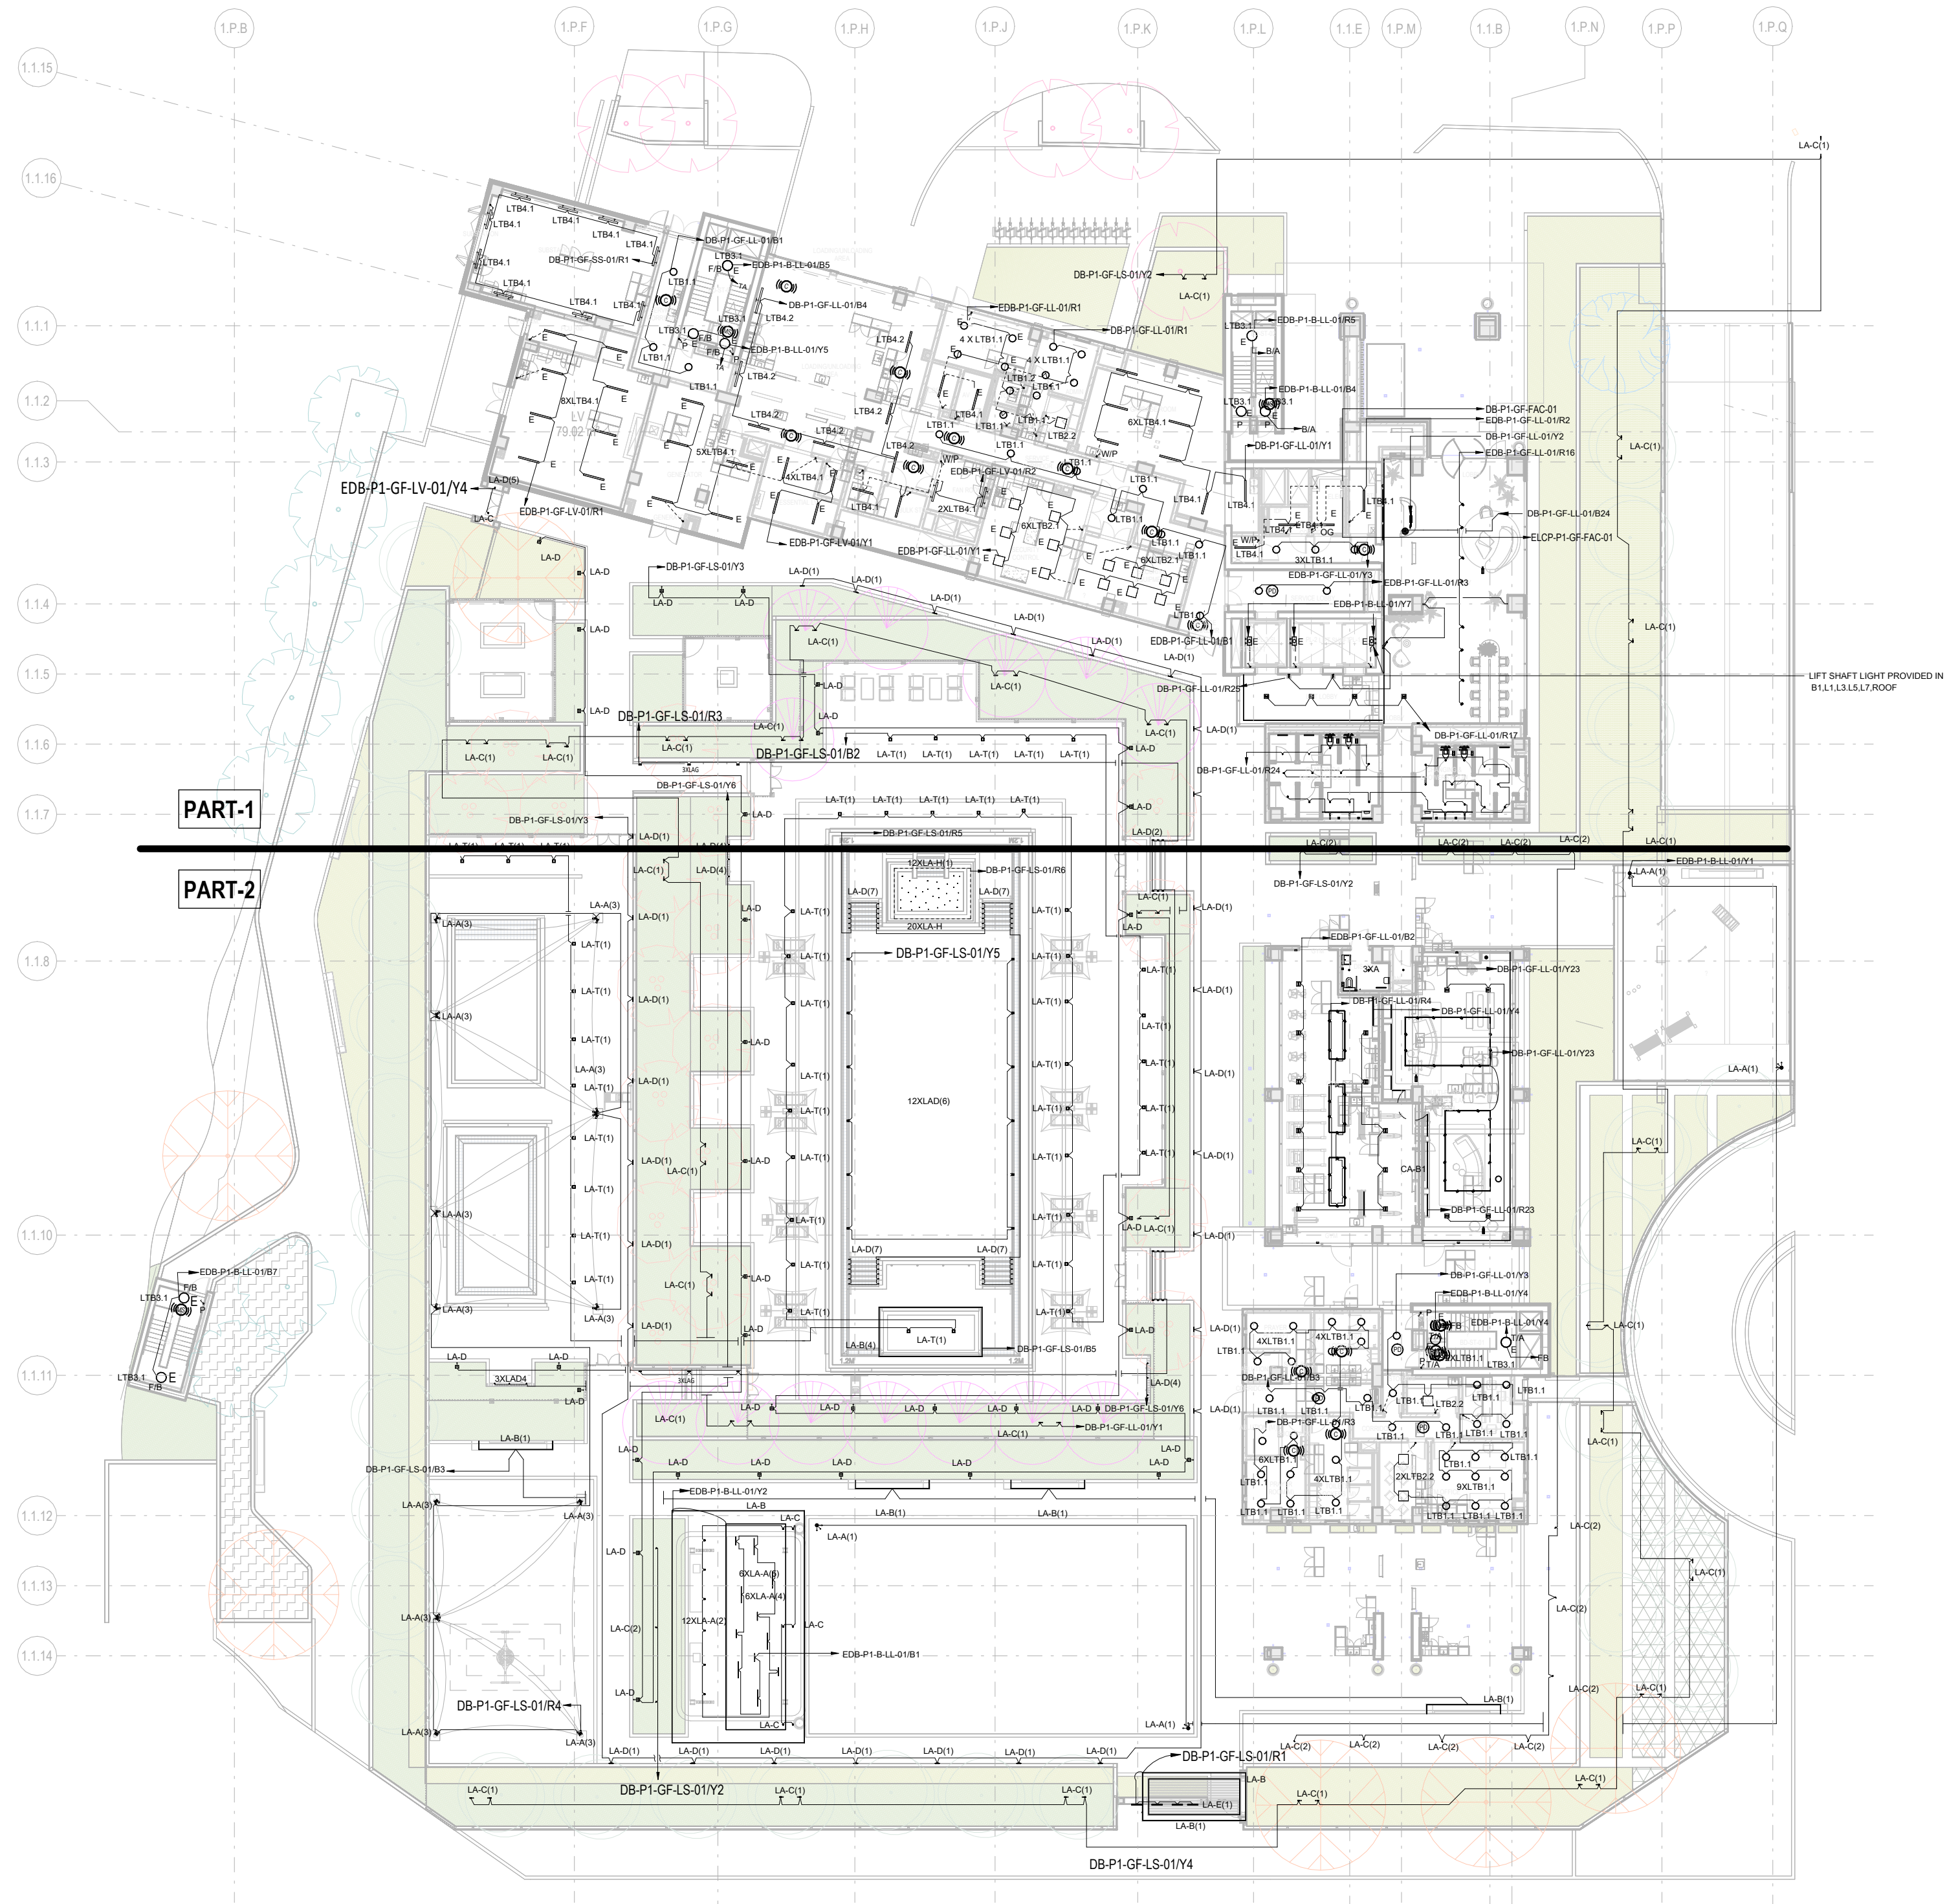

1 PODIUM - GROUND FLOOR LIGHTING LAYOUT
1010 1 : 300

- GENERAL NOTES:
1. THIS DRAWING IS THE COPYRIGHT OF MIRAGE AND MUST NOT BE RETAINED, COPIED, OR USED WITHOUT THE ABOVE CONSULTANTS' AUTHORITY.
 2. DO NOT SCALE FROM THE DRAWINGS. CHECK ALL DIMENSIONS ON SITE AND NOTIFY THE ENGINEER OF ANY DISCREPANCIES BEFORE PROCEEDING WITH WORK.
 3. ALL DIMENSIONS ARE IN MILLIMETERS AND LEVELS IN METERS, UNLESS NOTED OTHERWISE. ALL DIMENSIONS TO BE VERIFIED ON SITE AND APPROVED BY THE ENGINEER.
 4. THIS DRAWING SHOULD BE READ IN CONJUNCTION WITH OTHER RELEVANT ARCHITECTURAL, STRUCTURAL, MECHANICAL, ELECTRICAL, CIVIL DRAWINGS, AND ALL RELEVANT SECTIONS OF THE SPECIFICATIONS.
 5. THE FLOOR LEVEL 0.000 IS EQUAL TO +6.50 M RELATIVE TO THE DM DATUM LEVEL.

BUILDING PLOT NUMBER
3262969 - 01
KEY PLAN

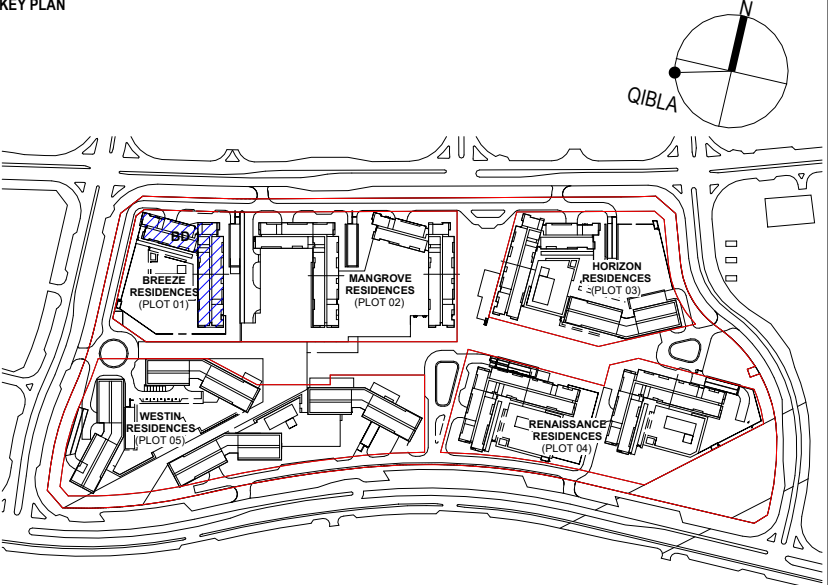

REV	DESCRIPTION	DATE	APPROVED BY
A	100% DETAIL DESIGN	11-SEP-2026	AV

PROJECT STAGE
DETAIL DESIGN

SHEET STATUS
FOR APPROVAL

CLIENT



LEAD DESIGN CONSULTANT AND ARCHITECT OF RECORD
mirage
Mirage Inc Consultants, PO Box 54054, Emara Business Park, Office 302, Dubai, UAE
T: +971 4 453 9835 W: www.mirageglobal.com

SUBCONSULTANT

DISCIPLINE
ELECTRICAL

PROJECT NAME
DUBAI CREEK GARDENS
BREEZE RESIDENCES (PLOT 01)
AL JADDAF, DUBAI
UNITED ARAB EMIRATES

SHEET NAME
PODIUM
GROUND FLOOR
LIGHTING LAYOUT OVERALL

SCALE		ORIGINAL SHEET SIZE	MIRAGE PROJECT NUMBER		
1 : 300		ISO A1 (841x594mm)	DES00044		
AUTHORITY DRAWING NO.	MIRAGE DRAWING NO.	DRAWN BY	CHECKED BY	REVISION	
E-00-1010	E-1010	MM	MC	A	
SHEET NUMBER 00044-DHCGP-MRG-PL1-PDM-DWG-ELE-1010					